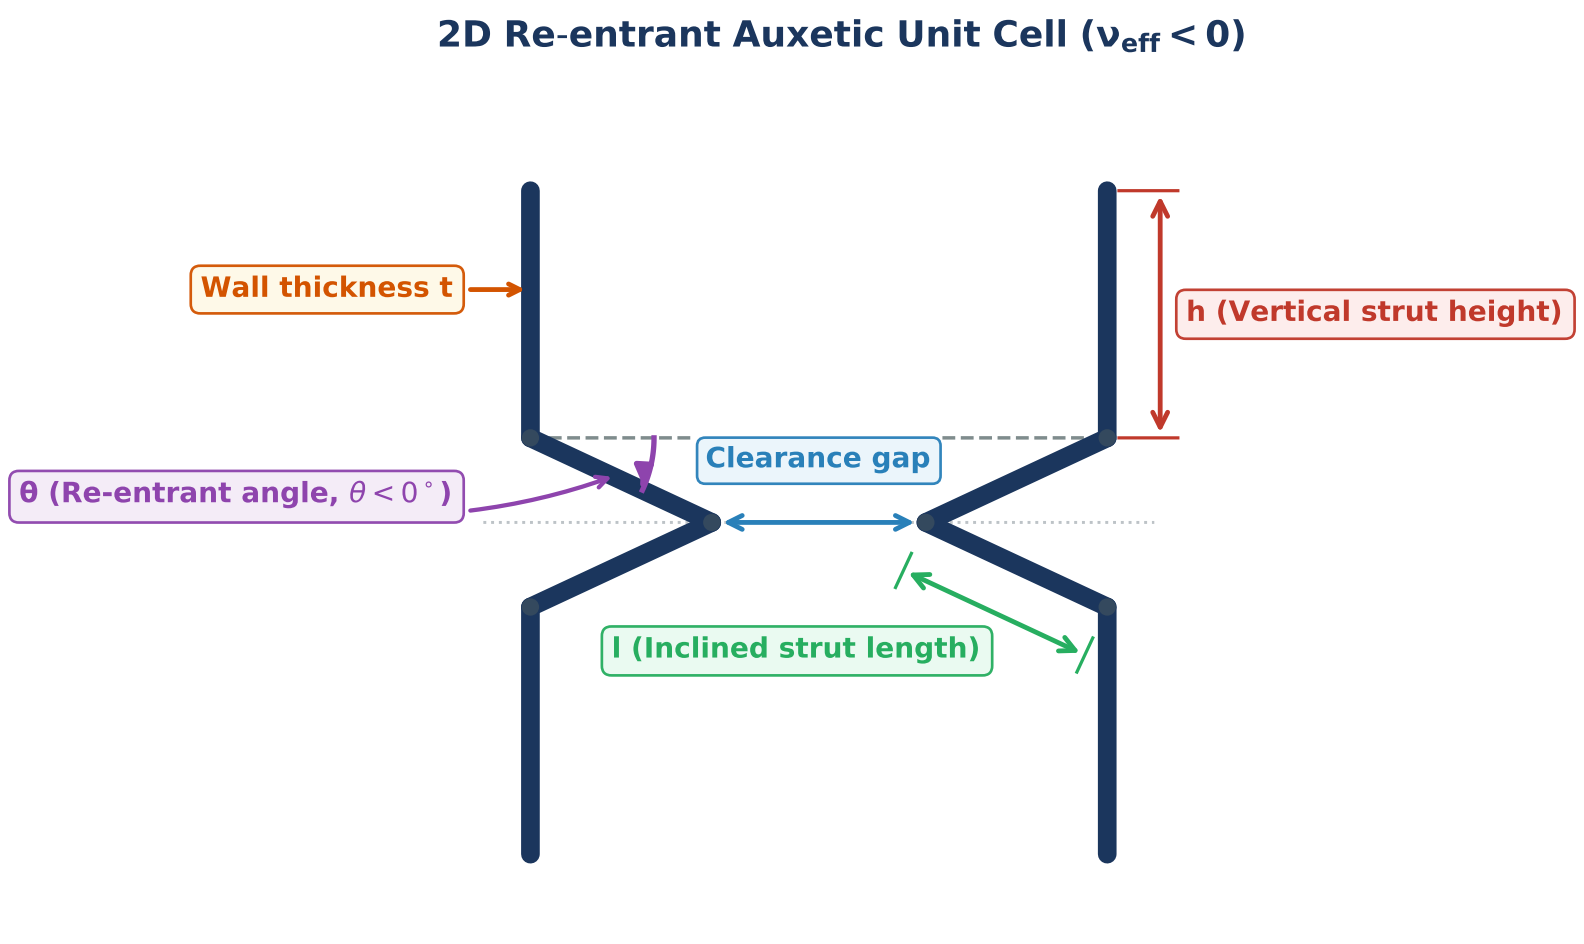
2D Re-entrant Auxetic Unit Cell ($\nu_{eff} < 0$)
Wall thickness t
h (Vertical strut height)
θ (Re-entrant angle, $\theta < 0^\circ$)
Clearance gap
l (Inclined strut length)